


SHOP MATERIAL LIST FOR ASSEMBLIES				
Mark	Size	No.	Length (m)	Weight Each (kg)
GUT1	CLOVIS_EAV_***	1	5398	18.35
GUT2	CLOVIS_EAV_***	1	5003	17.01
GUT3	CLOVIS_EAV_***	1	5003	17.01
GUT4	CLOVIS_EAV_***	1	5398	18.35

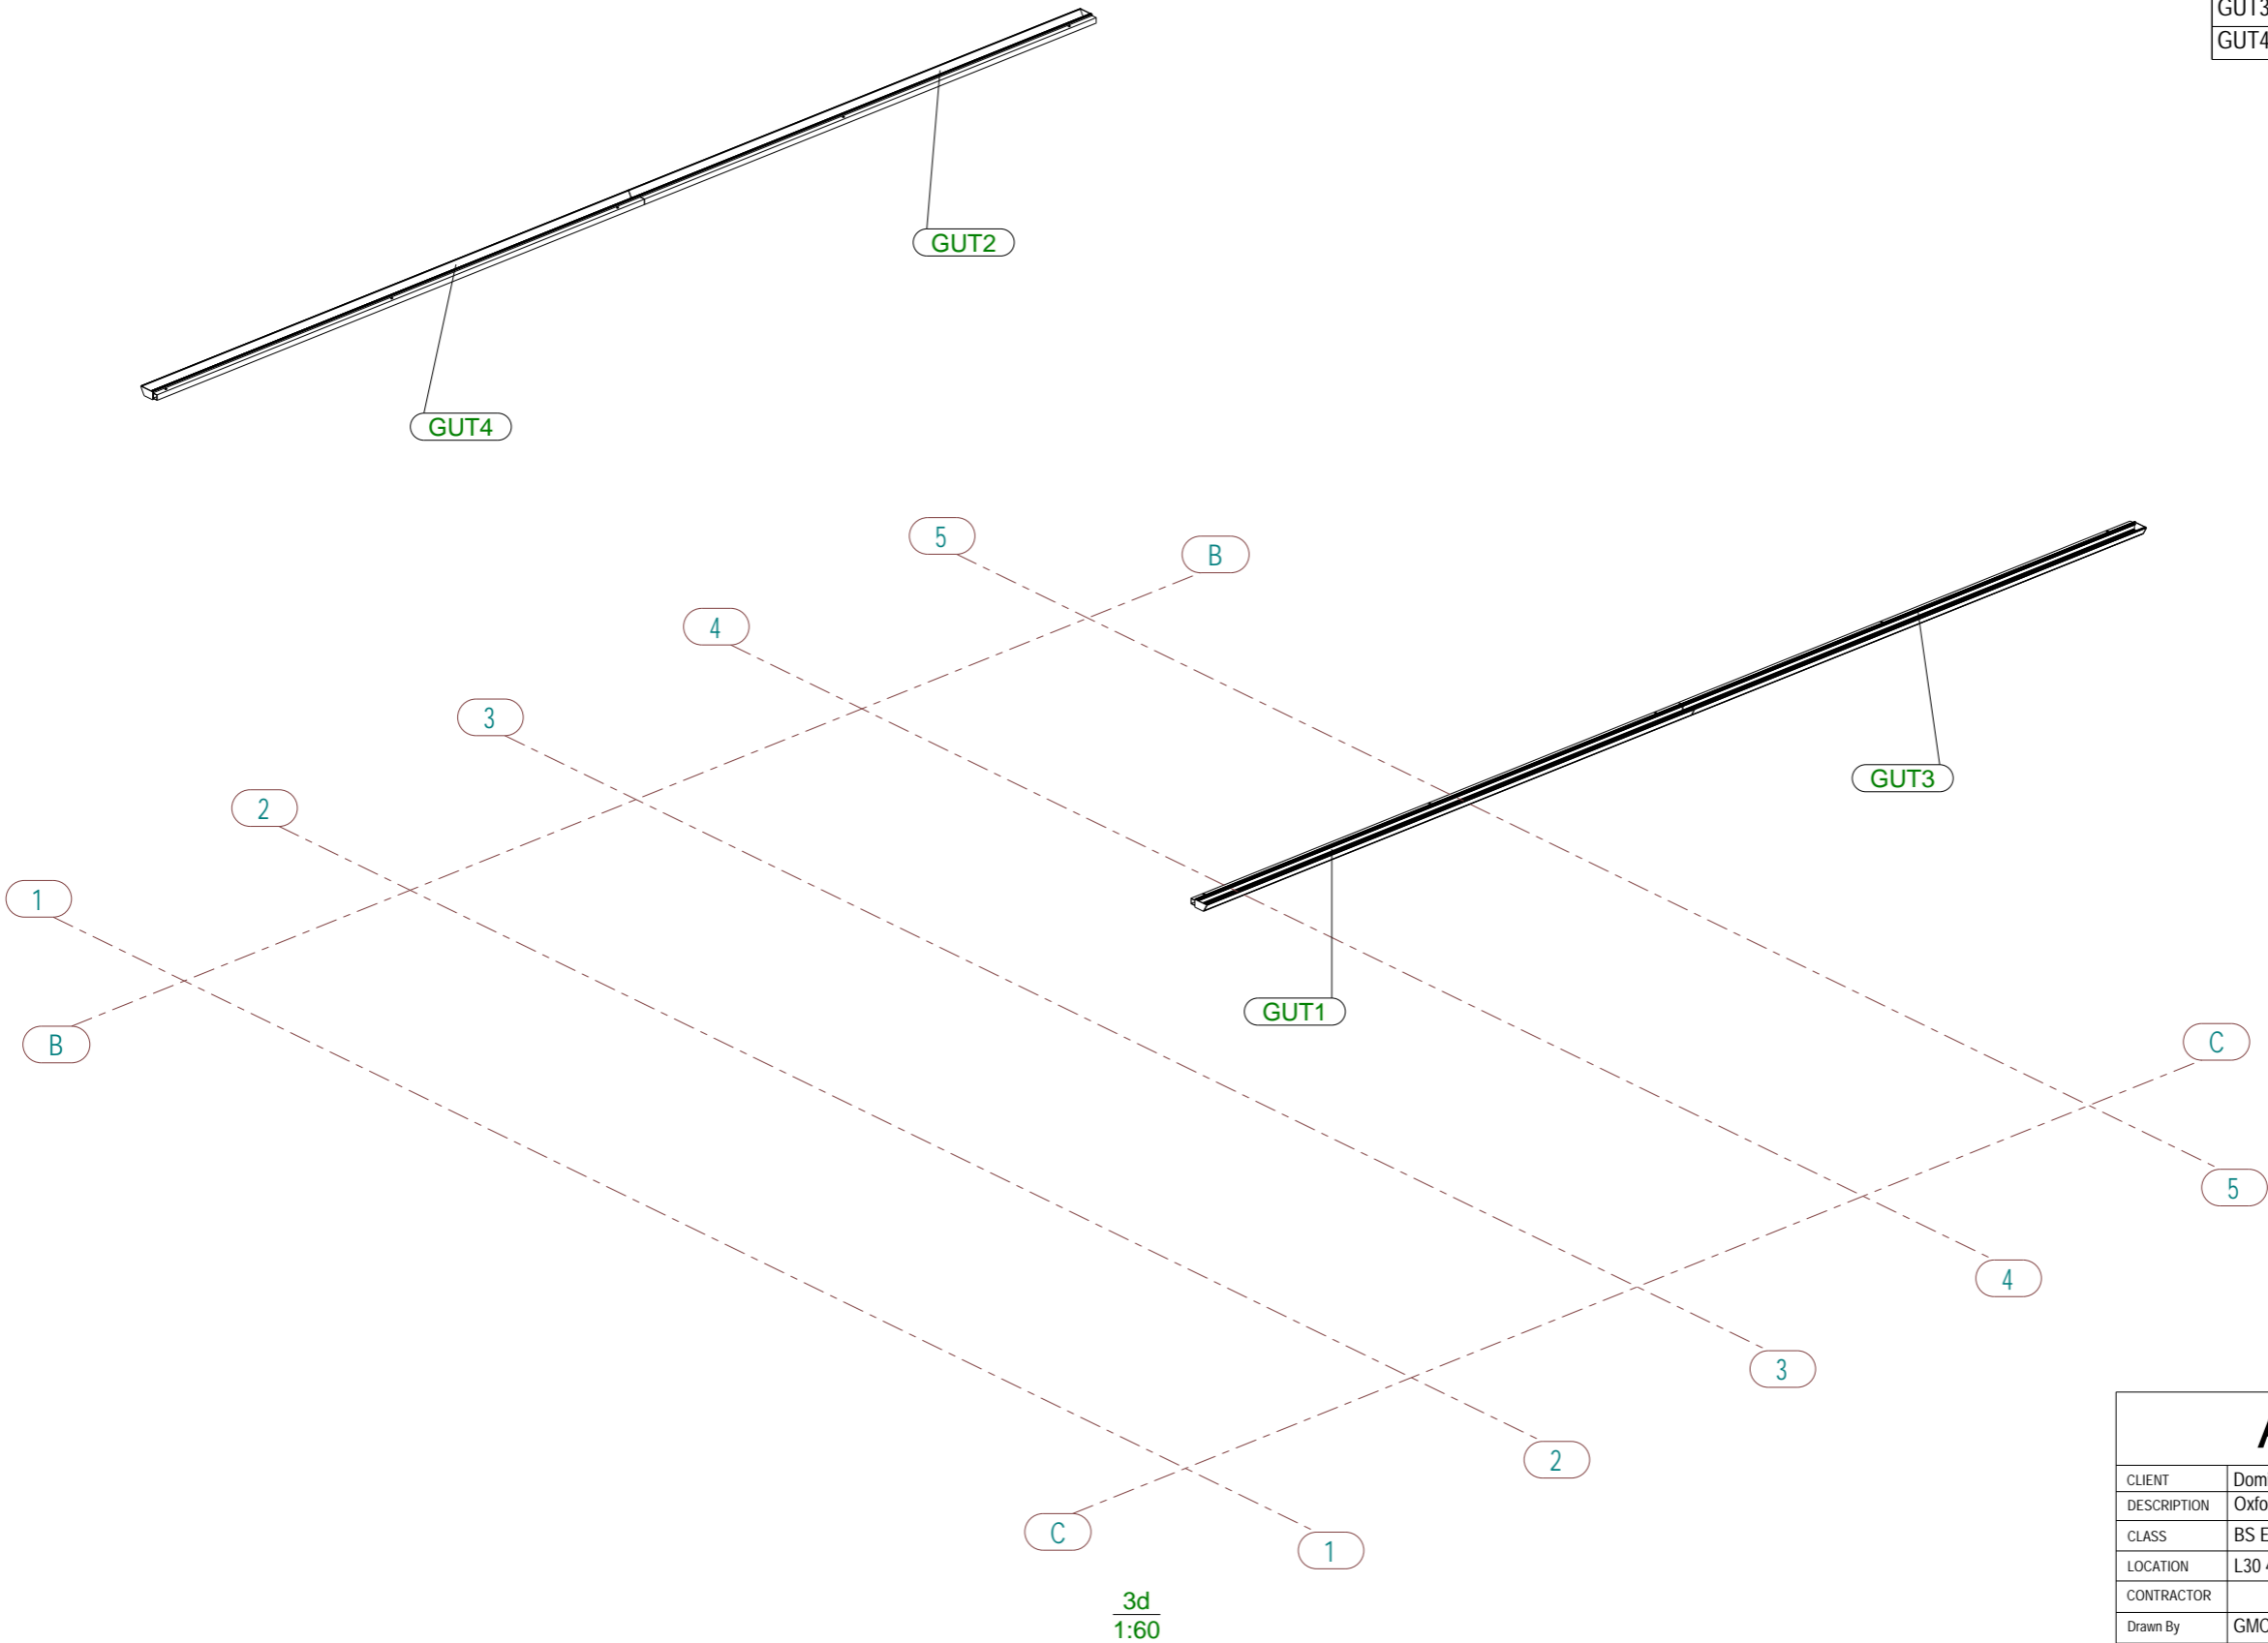

Approved				
CLIENT	Domino Printing			
DESCRIPTION	Oxford XL			
CLASS	BS EN 1090 Ex Class 2			
LOCATION	L30 4AJ			
CONTRACTOR				
Drawn By	GMC			
REVISION			JOB / ORDER NO: 704216	PLOT SIZE A3
DRAWN	CHECKED	GA - Gutters - For inst		DRAWING NO:
GMC				
CLOVIS CANOPIES				
Branbridges Road, East Peckham, TONBRIDGE, Kent TN12 5HH				
Tel: 01622 873900				
www.clovis-canopies.co.uk				
DO NOT SCALE FROM DRAWING - IF IN DOUBT ASK - ALL RIGHTS RESERVED				